

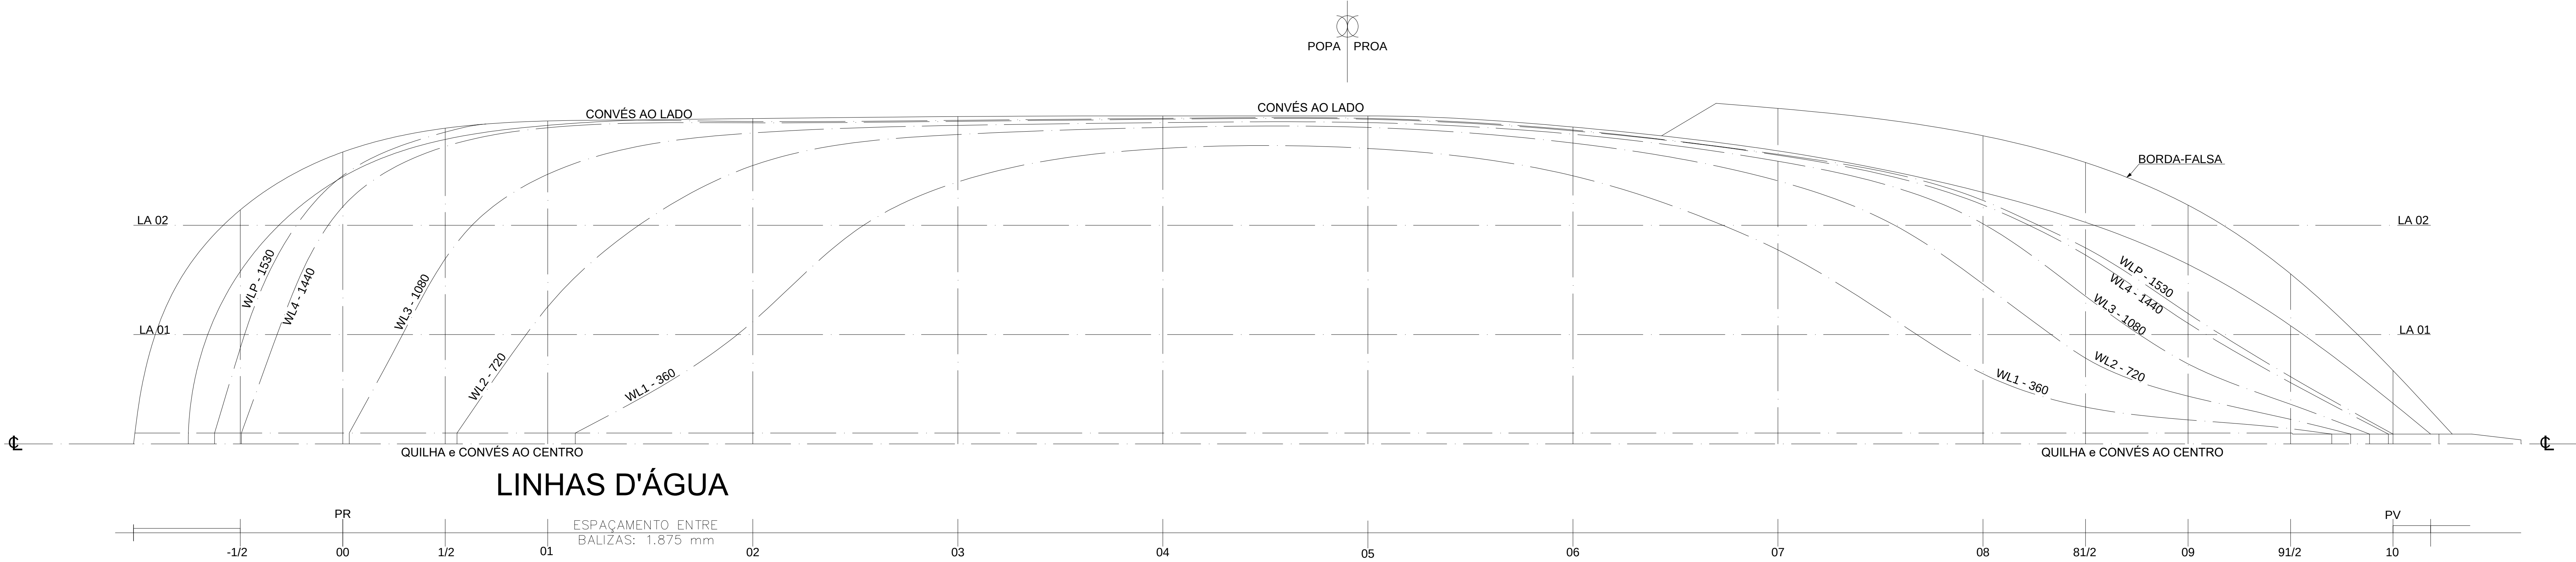


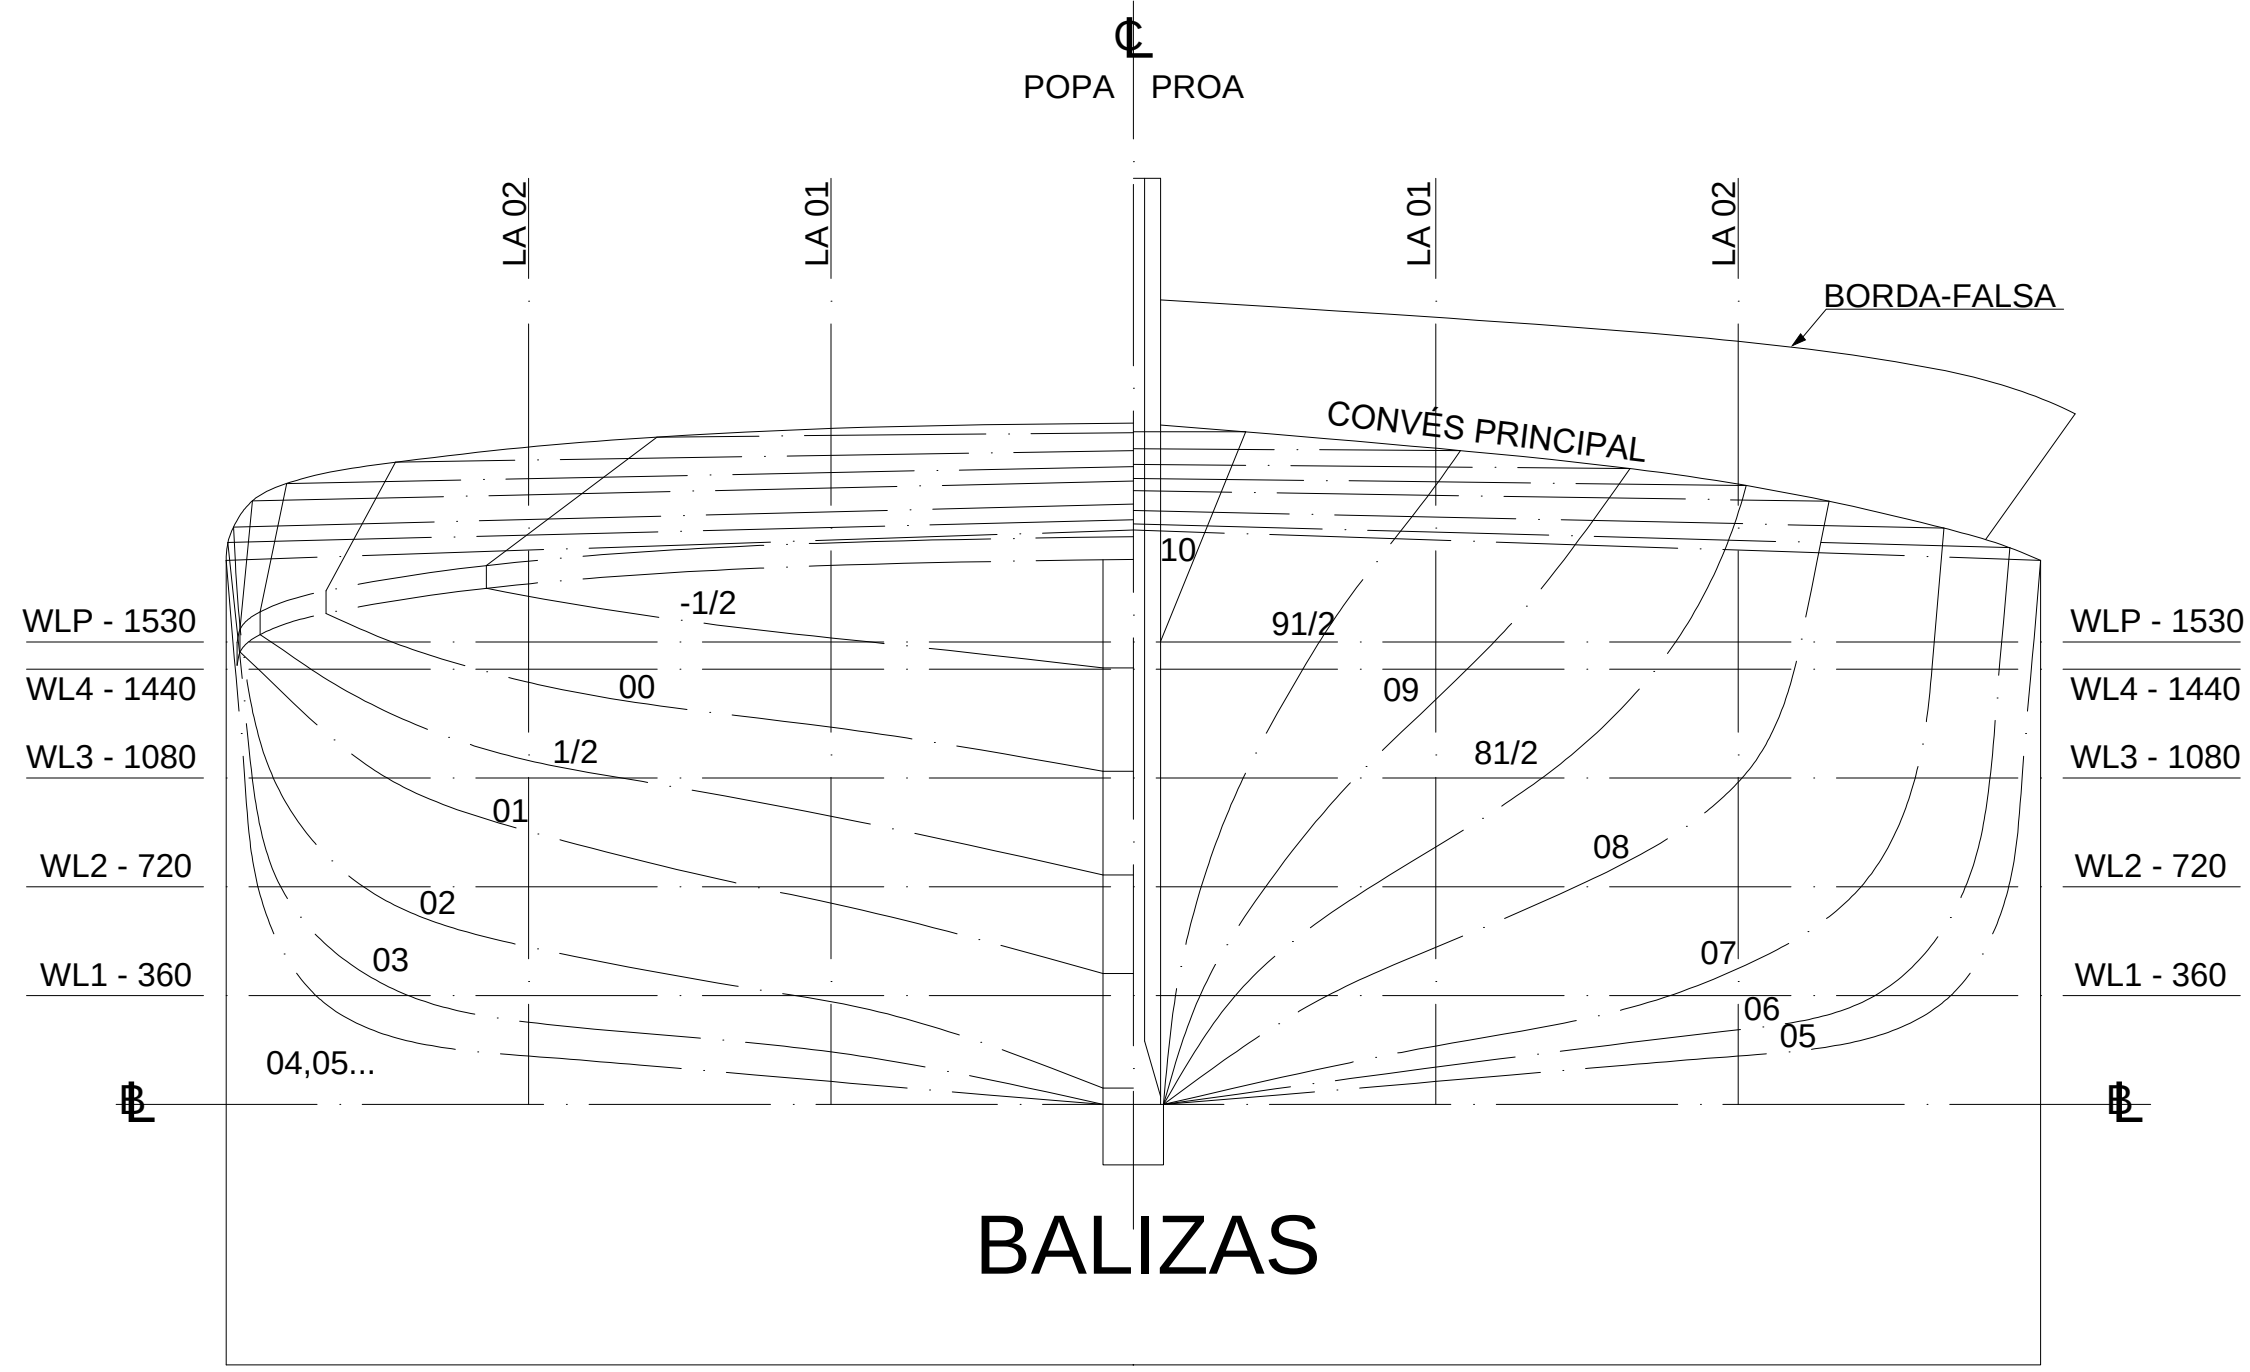

CARACTERÍSTICAS PRINCIPAIS
COMPRIMENTO TOTAL = 22,000 m
COMPRIMENTO TOTAL + APÊNDICES = 17,550 m
COMPRIMENTO ENTRE PERPENDICULARES = 18,750 m
BOCA MOLDADA = 6,000 m
PONTAL MOLDADO = 1,800 m
CALADO DE PROJETO = 1,530 m

OBSERVAÇÕES
TODAS AS MEDIDAS ESTÃO EM MILÍMETROS
A LINHA DE REFERÊNCIA DOS CALADOS É A LINHA DE BASE

REV	DESCRIÇÃO	DATA	ELAB.	APROV.
C				
B				
A				
INICIAL	Emissão inicial	NOVEMBRO/2020	IG	IG

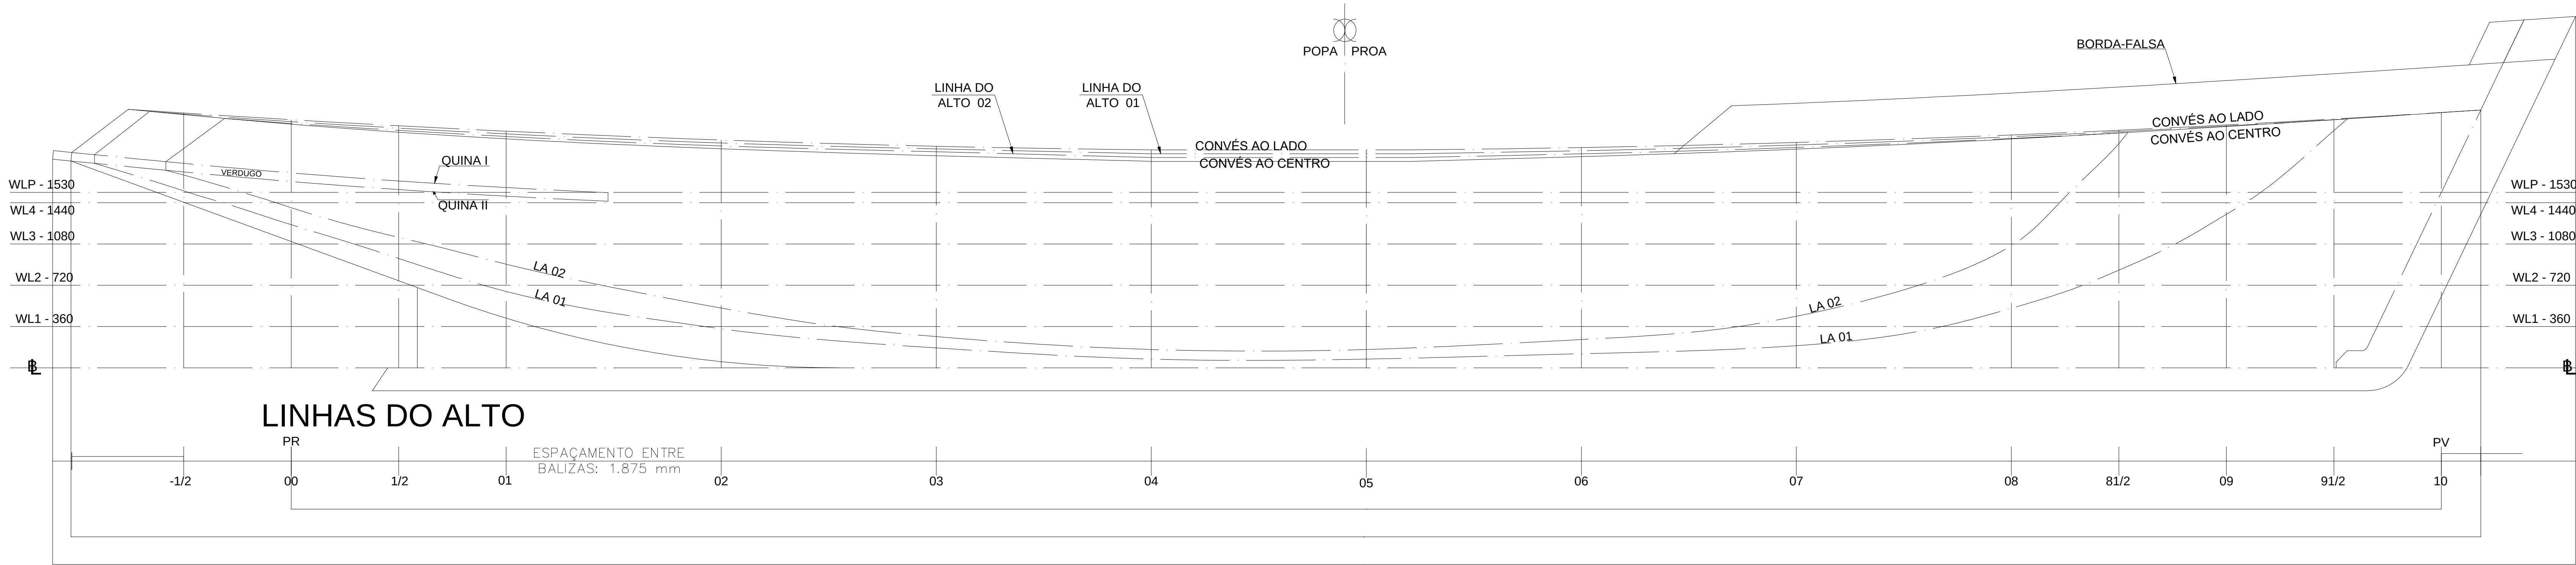

IV - CONSULTORIA E ENGENHARIA NAVAL
Telefone: (93) 9844600568
E-mail: iv.naval@outlook.com

PLANO
PLANO DE LINHAS

EMBARCAÇÃO
DONNA MARIANA

ARMADOR
SALEMA NOGUEIRA BECHARA

ESTALEIRO CONSTRUTOR
SALEMA NOGUEIRA BECHARA

Nº PROJETO 06.LIV-2020 **TIPO** PASSAGEIRO/CARGA

PROJETISTA ÍTALO G.S. **REVISÃO** **DATA** 03/11/2020

RESP. TÉCNICO ÍTALO GUAYIBA SANTOS - CREA PA 15342038-36 **ESCALA** 1:25

