
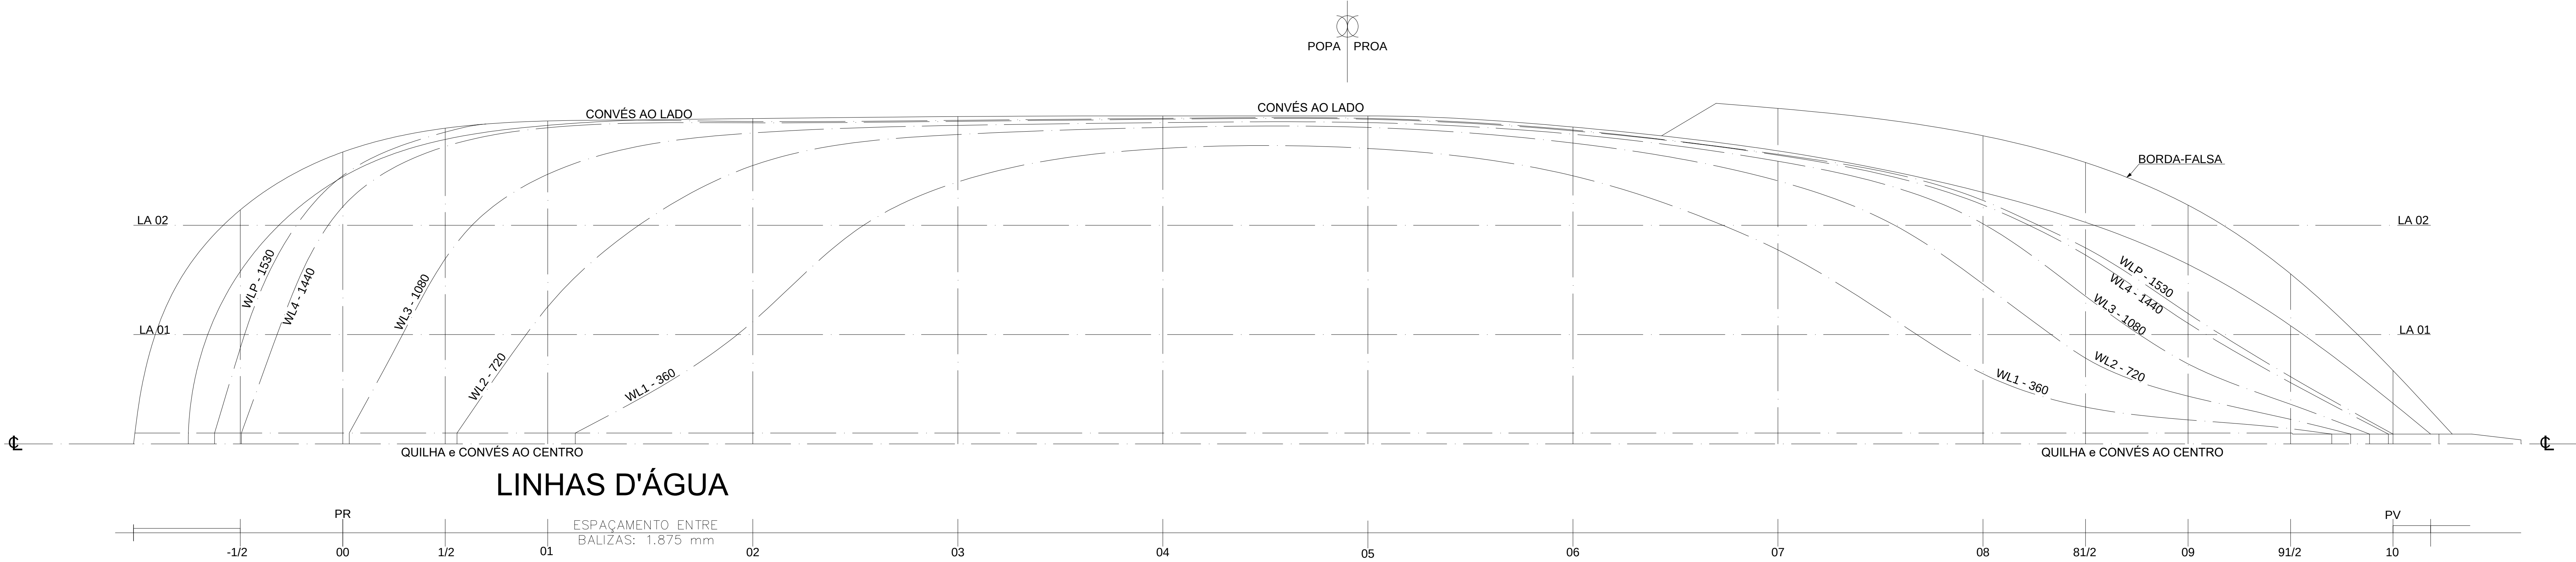
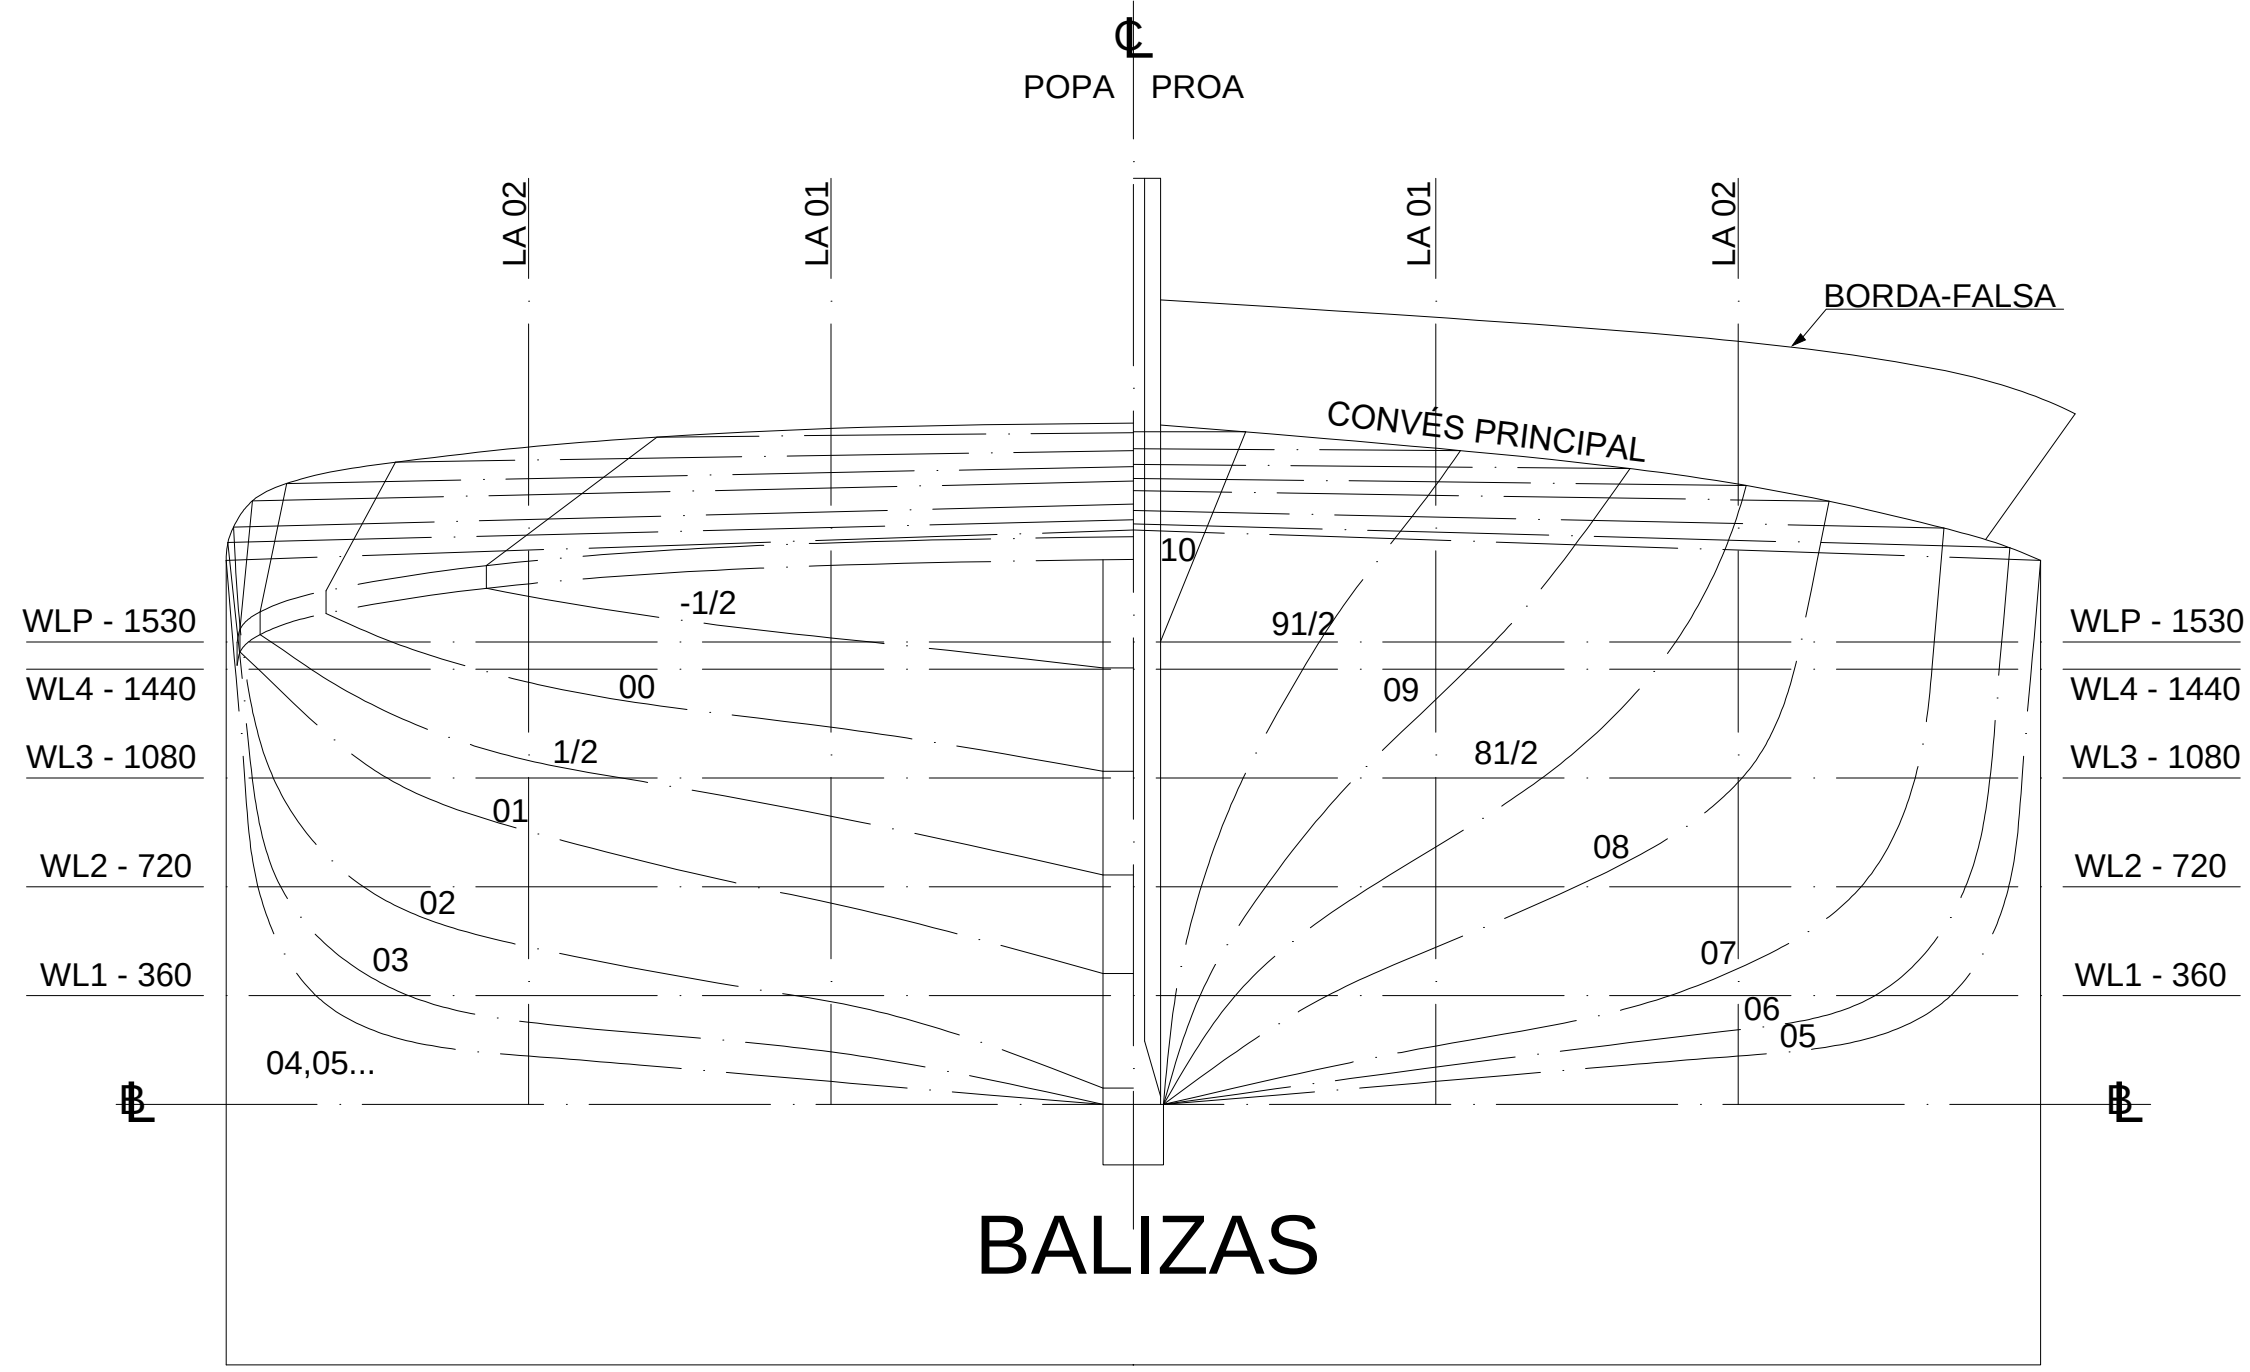


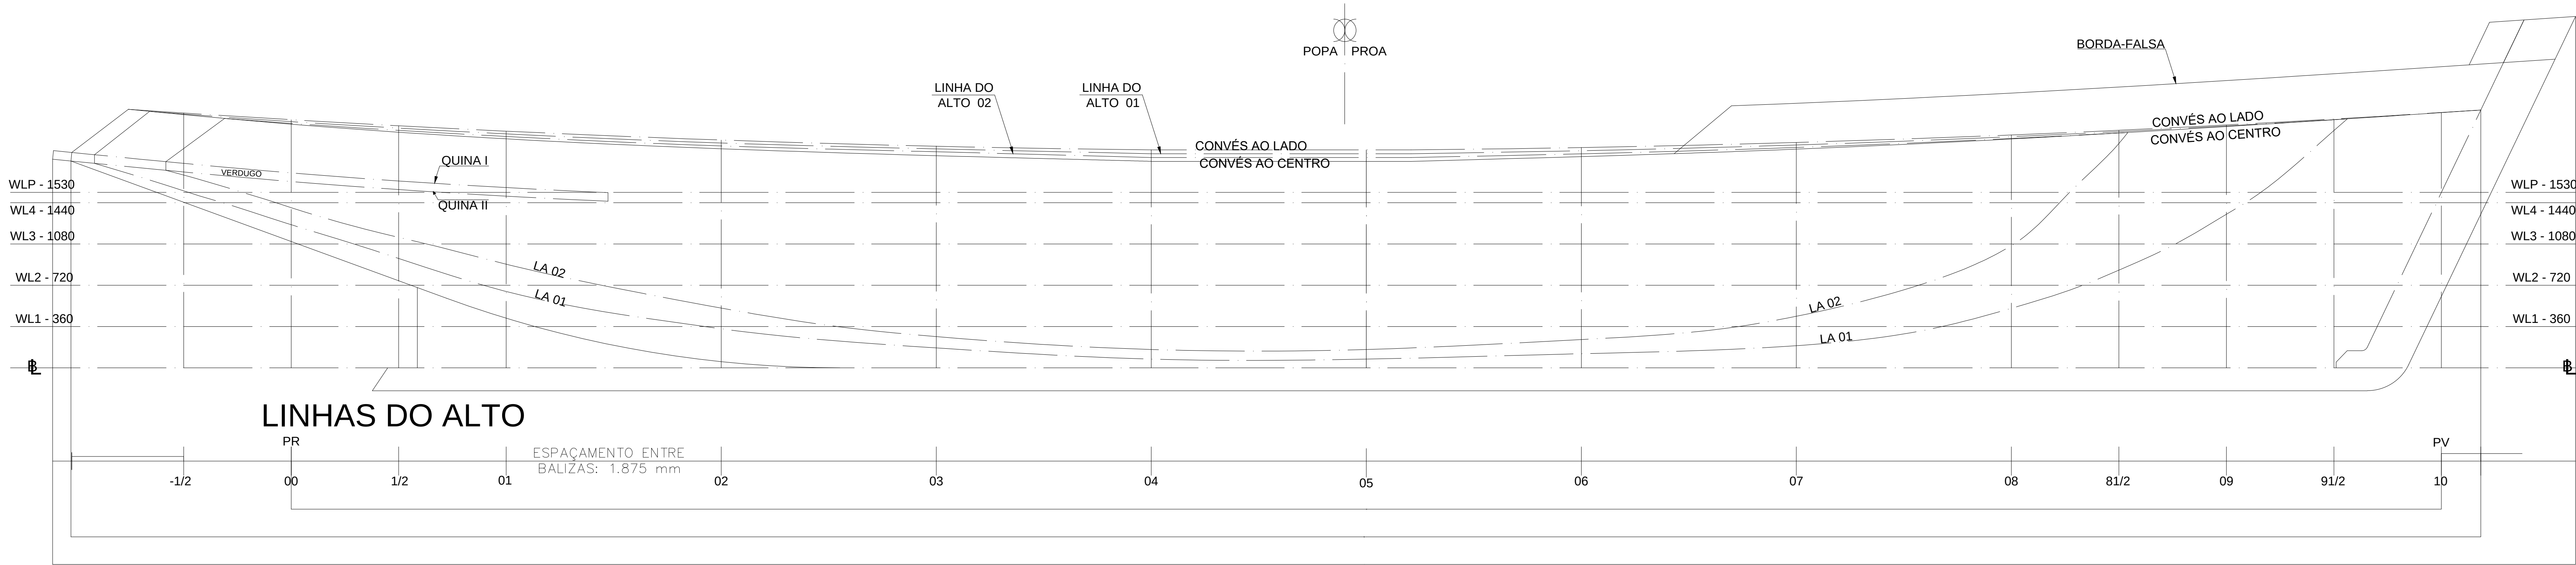

CARACTERÍSTICAS PRINCIPAIS
COMPRIMENTO TOTAL = 22,000 m
COMPRIMENTO TOTAL + APÊNDICES = 17,550 m
COMPRIMENTO ENTRE PERPENDICULARES = 18,750 m
BOCA MOLDADA = 6,000 m
PONTAL MOLDADO = 1,800 m
CALADO DE PROJETO = 1,530 m

OBSERVAÇÕES
TODAS AS MEDIDAS ESTÃO EM MILÍMETROS
A LINHA DE REFERÊNCIA DOS CALADOS É A LINHA DE BASE

REV	DESCRIÇÃO	DATA	ELAB.	APROV.
C				
B				
A				

INICIAL	Emissão inicial	NOVEMBRO/2020	IG	IG

IV - CONSULTORIA E ENGENHARIA NAVAL
Telefone: (93) 9844600568
E-mail: iv.naval@outlook.com

PLANO
PLANO DE LINHAS

EMBARCAÇÃO
DONNA MARIANA

ARMADOR
SALEMA NOGUEIRA BECHARA

ESTALEIRO CONSTRUTOR
SALEMA NOGUEIRA BECHARA

Nº PROJETO	06.LIV-2020	TIPO	PASSEGEIRO/CARGA
PROJETISTA	ÍTALO G.S	REVISÃO	
DATA	03/11/2020	ESCALA	1:25

RESP. TÉCNICO

ÍTALO GUARIBA SANTOS - CREA PA 15140208-36

