
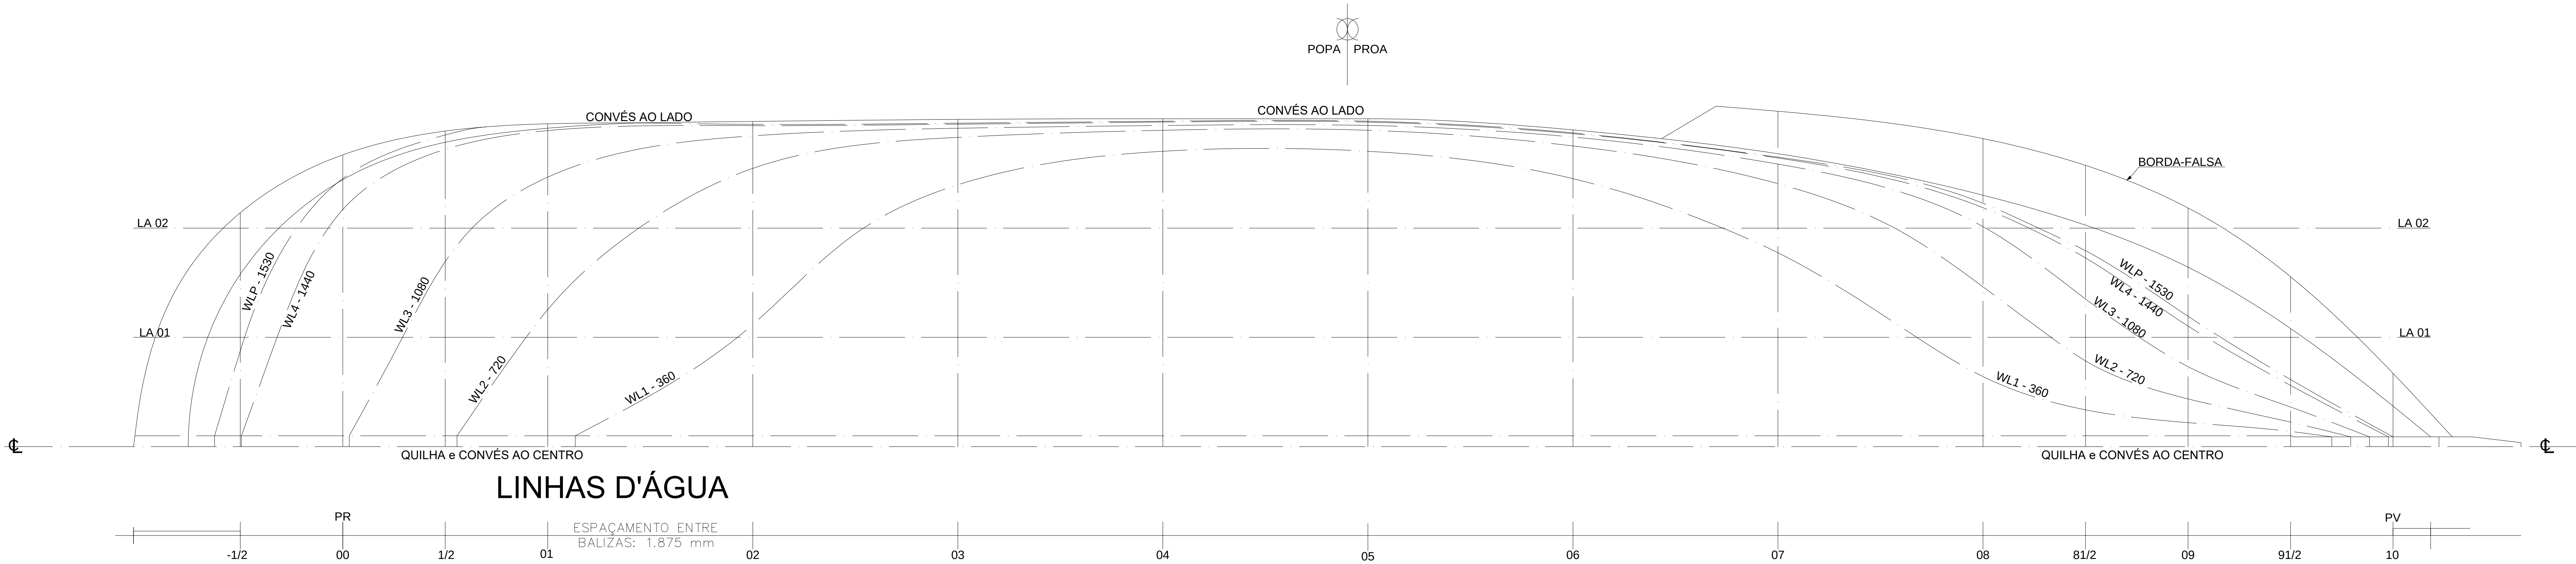
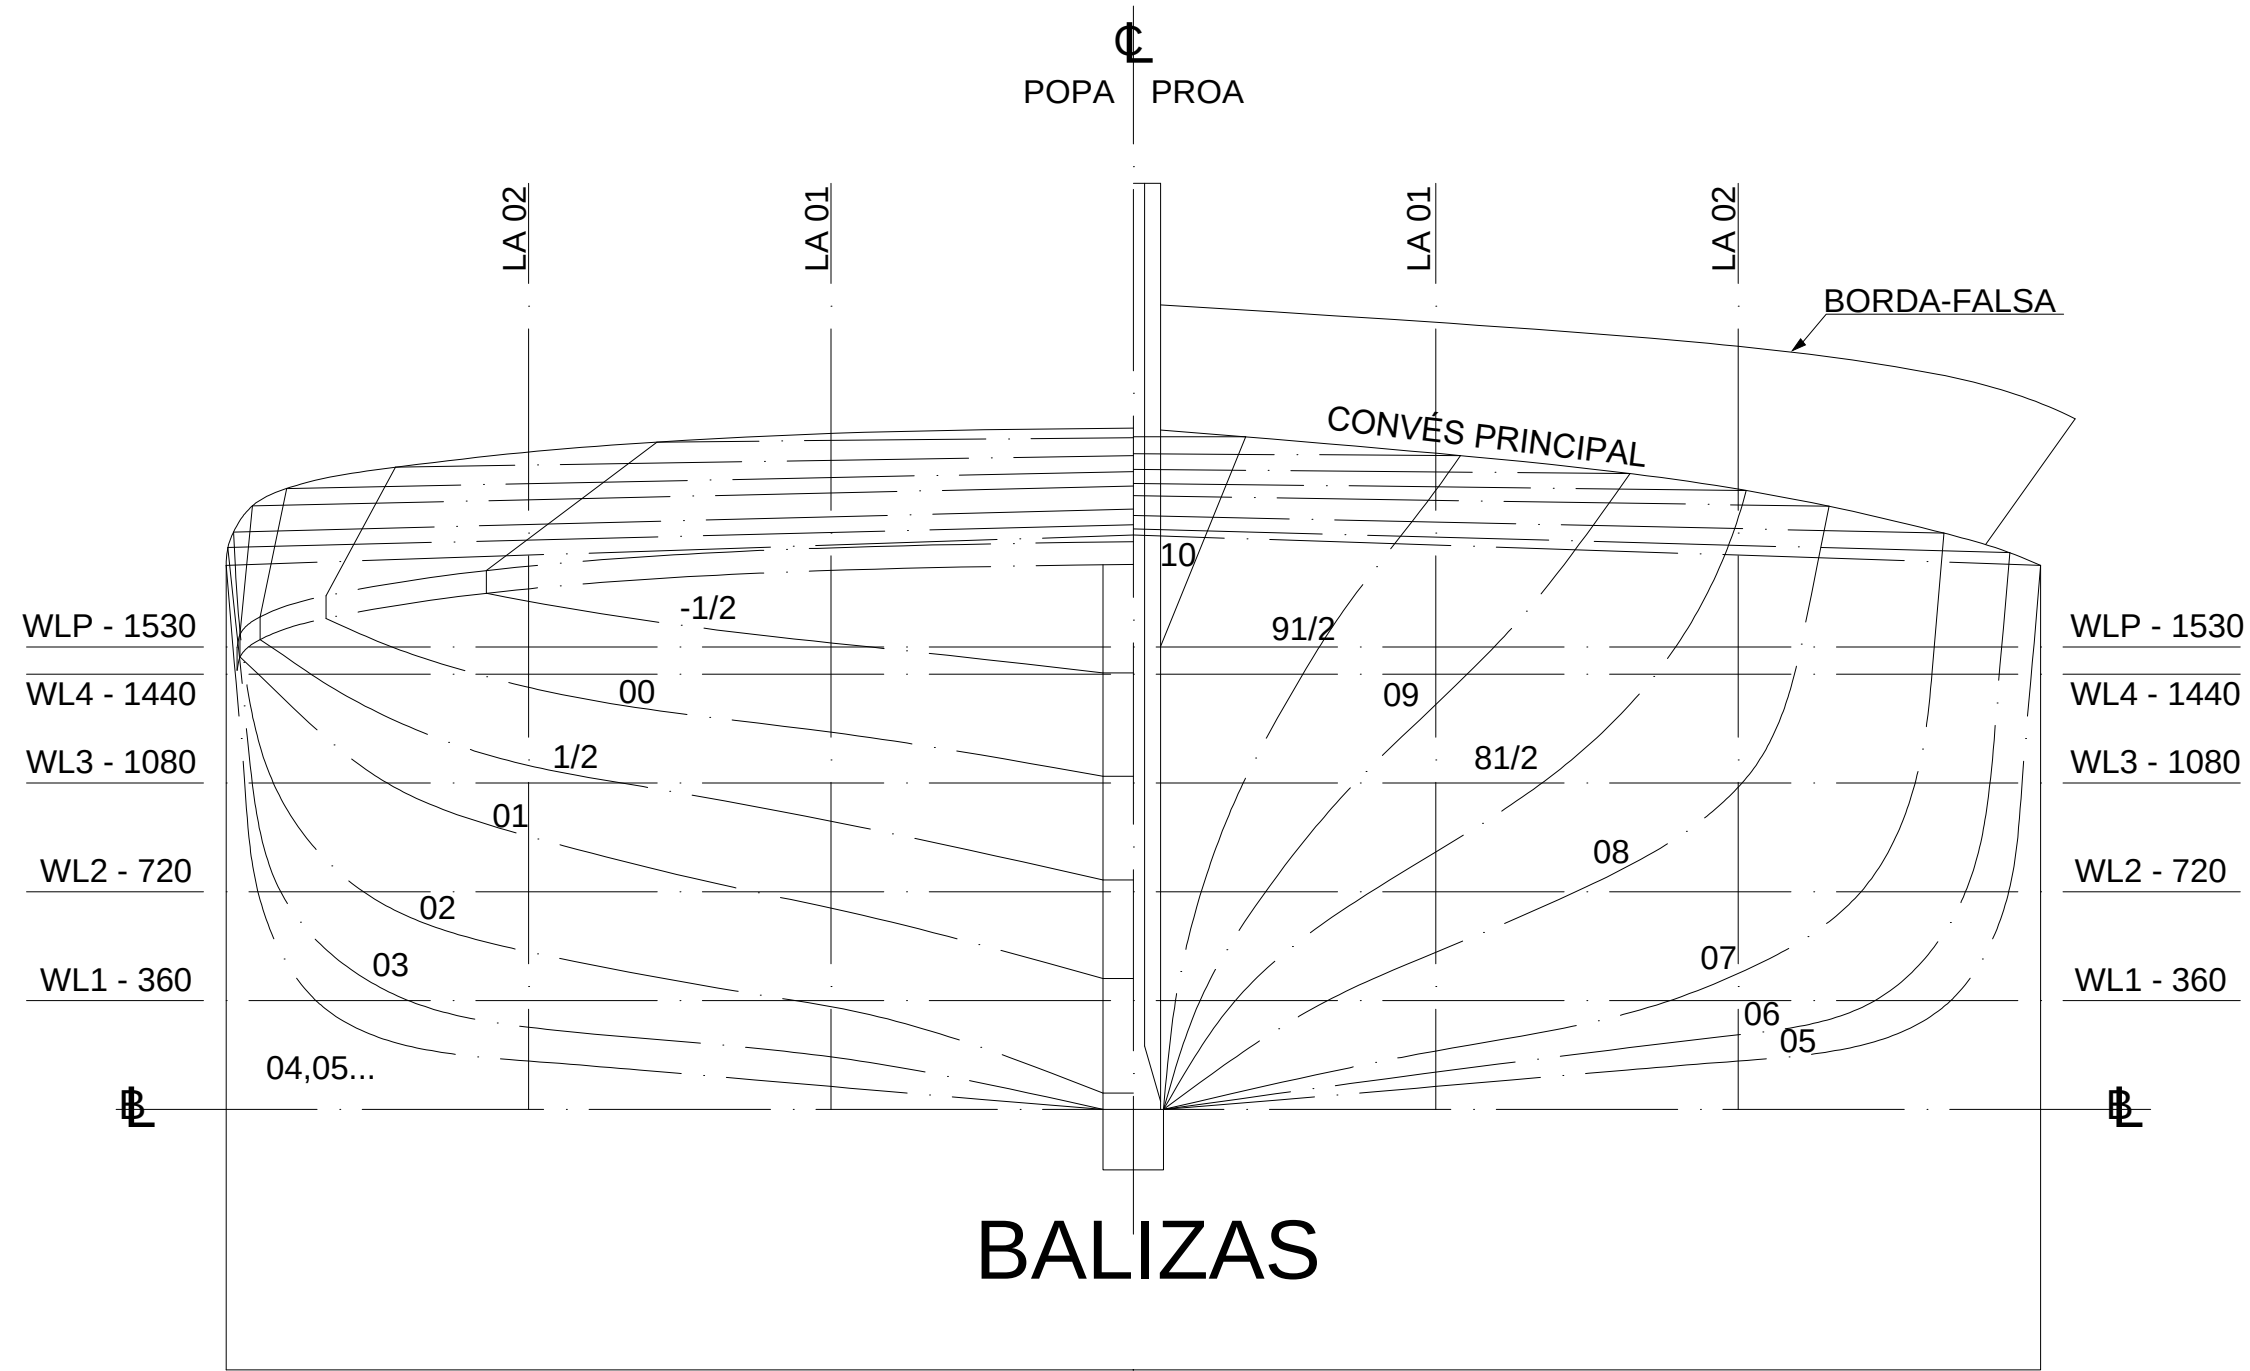


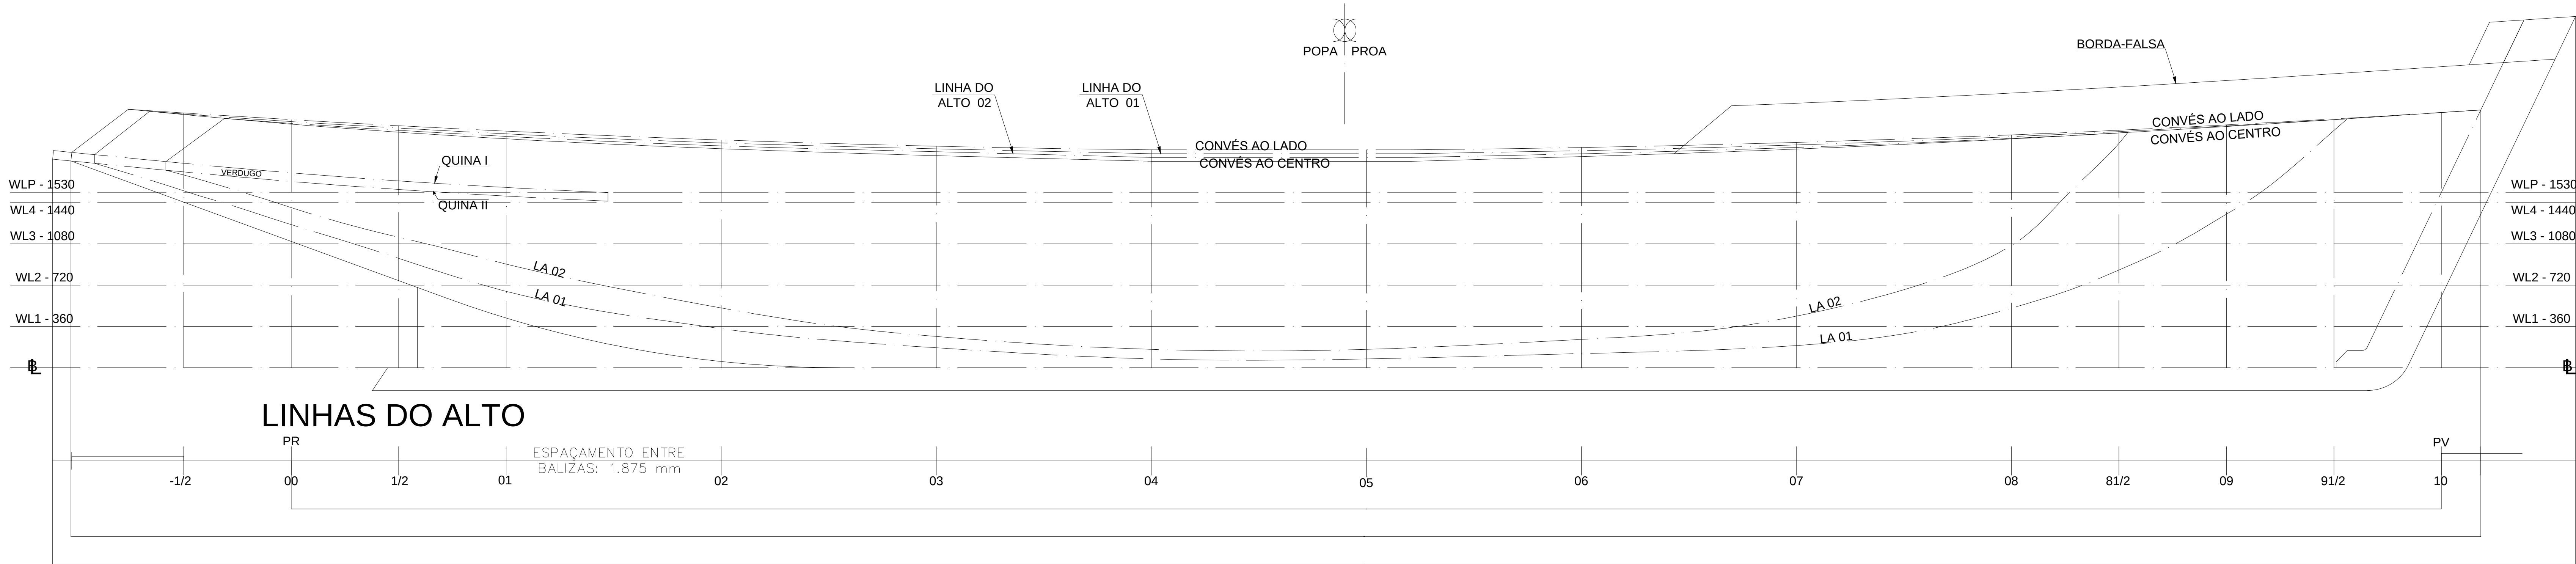

CARACTERÍSTICAS PRINCIPAIS

COMPRIMENTO TOTAL = 22,000 m
COMPRIMENTO TOTAL + APÊNDICES = 17,550 m
COMPRIMENTO ENTRE PERPENDICULARES = 18,750 m
BOCA MOLDADA = 6,000 m
PONTAL MOLDADO = 1,800 m
CALADO DE PROJETO = 1,530 m

OBSERVAÇÕES

TODAS AS MEDIDAS ESTÃO EM MILÍMETROS
A LINHA DE REFERÊNCIA DOS CALADOS É A LINHA DE BASE

REV	DESCRIÇÃO	DATA	ELAB.	APROV.
C				
B				
A				
INICIAL	Emissão inicial	NOVEMBRO/2020	IG	IG



IV - CONSULTORIA E ENGENHARIA NAVAL
Telefone: (93) 9844600568
E-mail: iv.naval@outlook.com

PLANO DE LINHAS

EMBARCAÇÃO
DONNA MARIANA

ARMADOR
SALEMA NOGUEIRA BECHARA

ESTALEIRO CONSTRUTOR
SALEMA NOGUEIRA BECHARA

Nº PROJETO
06.LIV-2020

TIPO
PASSAGEIRO/CARGA

PROJETISTA
ÍTALO G.S

REVISÃO
03/11/2020

RESP. TÉCNICO
ÍTALO GUAYIBA SANTOS - CREA PA 15340208-36

ESCALA
1:25