PRODUCED BY AN AUTODESK EDUCATIONAL PRODUCT

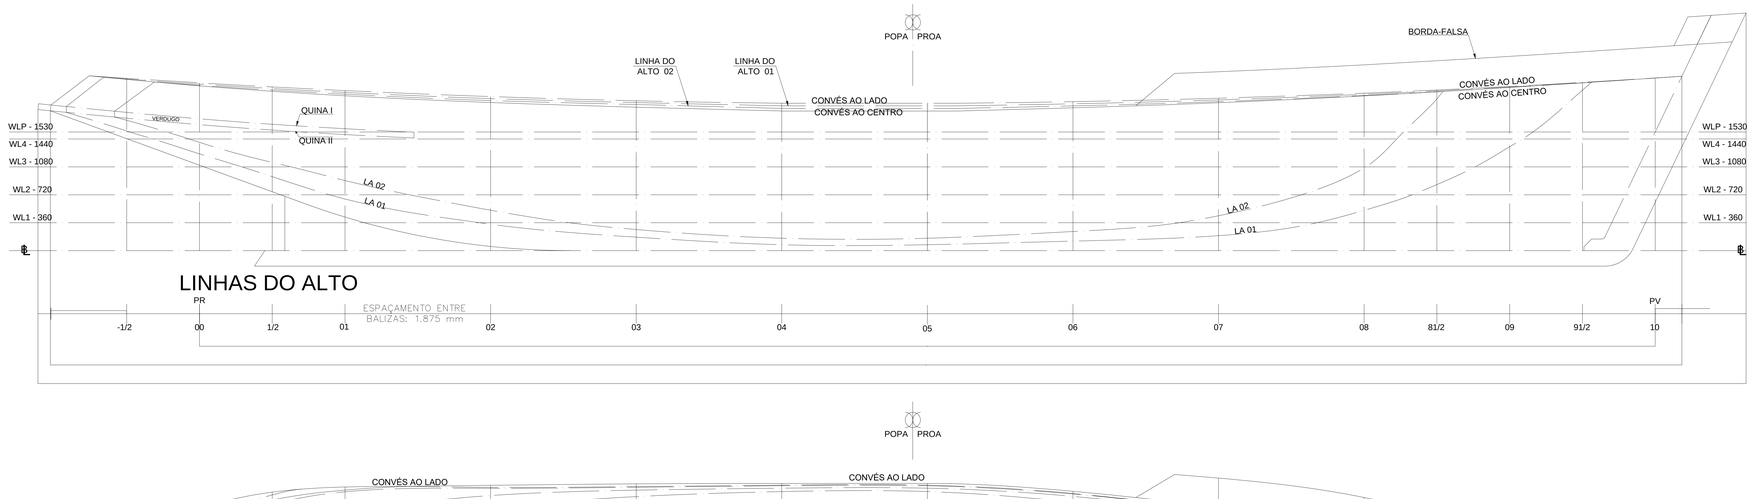

LINHAS DO ALTO

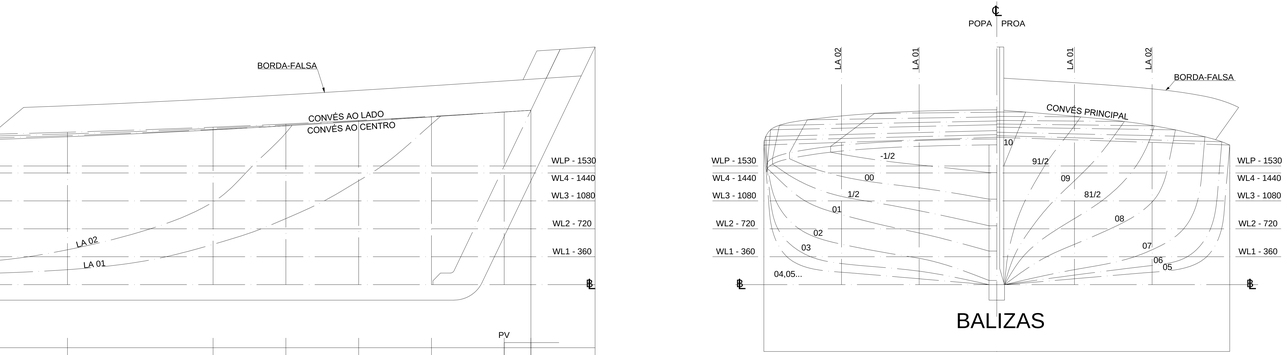

BALIZAS

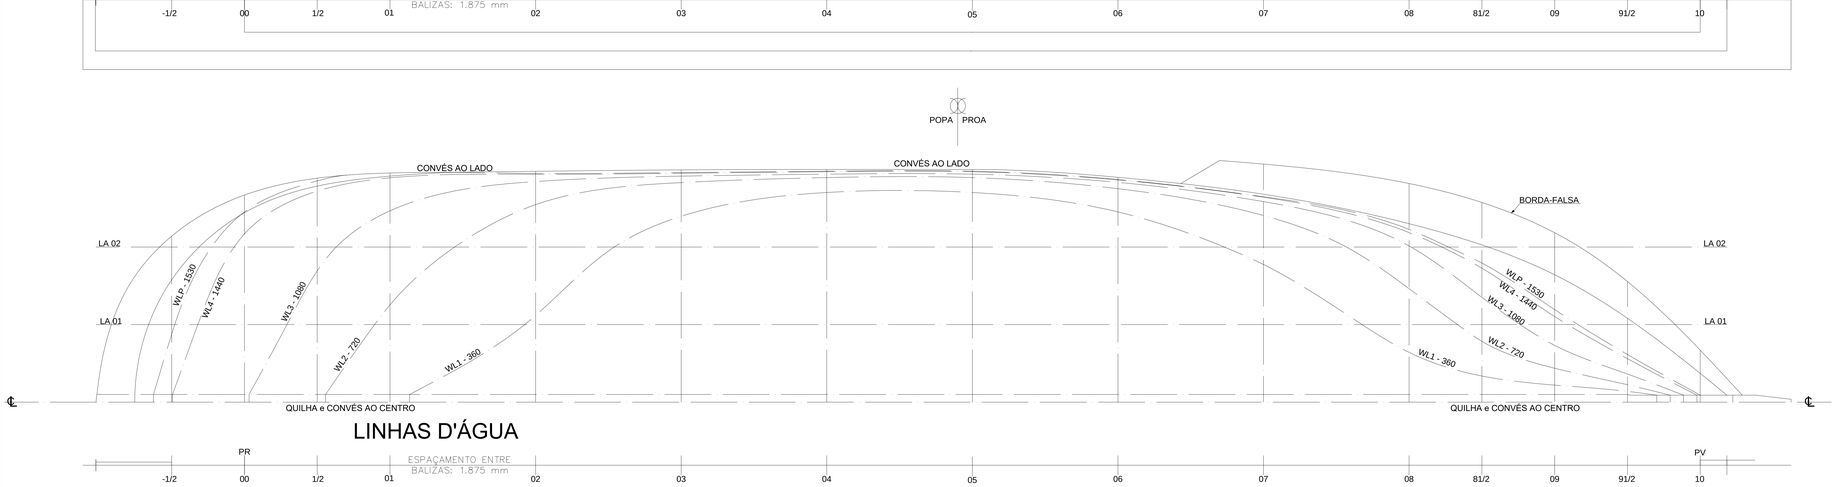

LINHAS D'ÁGUA

CARACTERÍSTICAS PRINCIPAIS

COMPRIMENTO TOTAL = 22,000 m
COMPRIMENTO TOTAL + APENDICES = 17,550 m
COMPRIMENTO ENTRE PERPENDICULARES = 18,750 m
BOCA MOLDADA = 6,000 m
PONTAL MOLDADO = 1,800 m
CALADO DE PROJETO = 1,530 m

OBSERVAÇÕES

TODAS AS MEDIDAS ESTÃO EM MILÍMETROS
A LINHA DE REFERÊNCIA DOS CALADOS É A LINHA DE BASE

REV	DESCRIÇÃO	DATA	ELAB.	APROV.
C				
B				
A				
INICIAL	Emissão inicial	30/NOVEMBRO/2020	IG	IG

IV - CONSULTORIA E ENGENHARIA NAVAL
Telefone: (93) 984660568
E-mail: iv.naval@outlook.com

PLANO
PLANO DE LINHAS

EMBARCAÇÃO
DONNA MARIANA

ARMADOR
SALEMA NOGUEIRA BECHARA

ESTALEIRO CONSTRUTOR
SALEMA NOGUEIRA BECHARA

Nº PROJETO	TIPO
06.LIV-2020	PASSAGEIRO/CARGA

PROJETISTA	REVISÃO	DATA
ÍTALO G.S		03/11/2020

RESP. TÉCNICO	ESCALA
ÍTALO GUANYBA SANTOS - CREA PA 1014033B-06	1:25

teste

PRODUCED BY AN AUTODESK EDUCATIONAL PRODUCT